
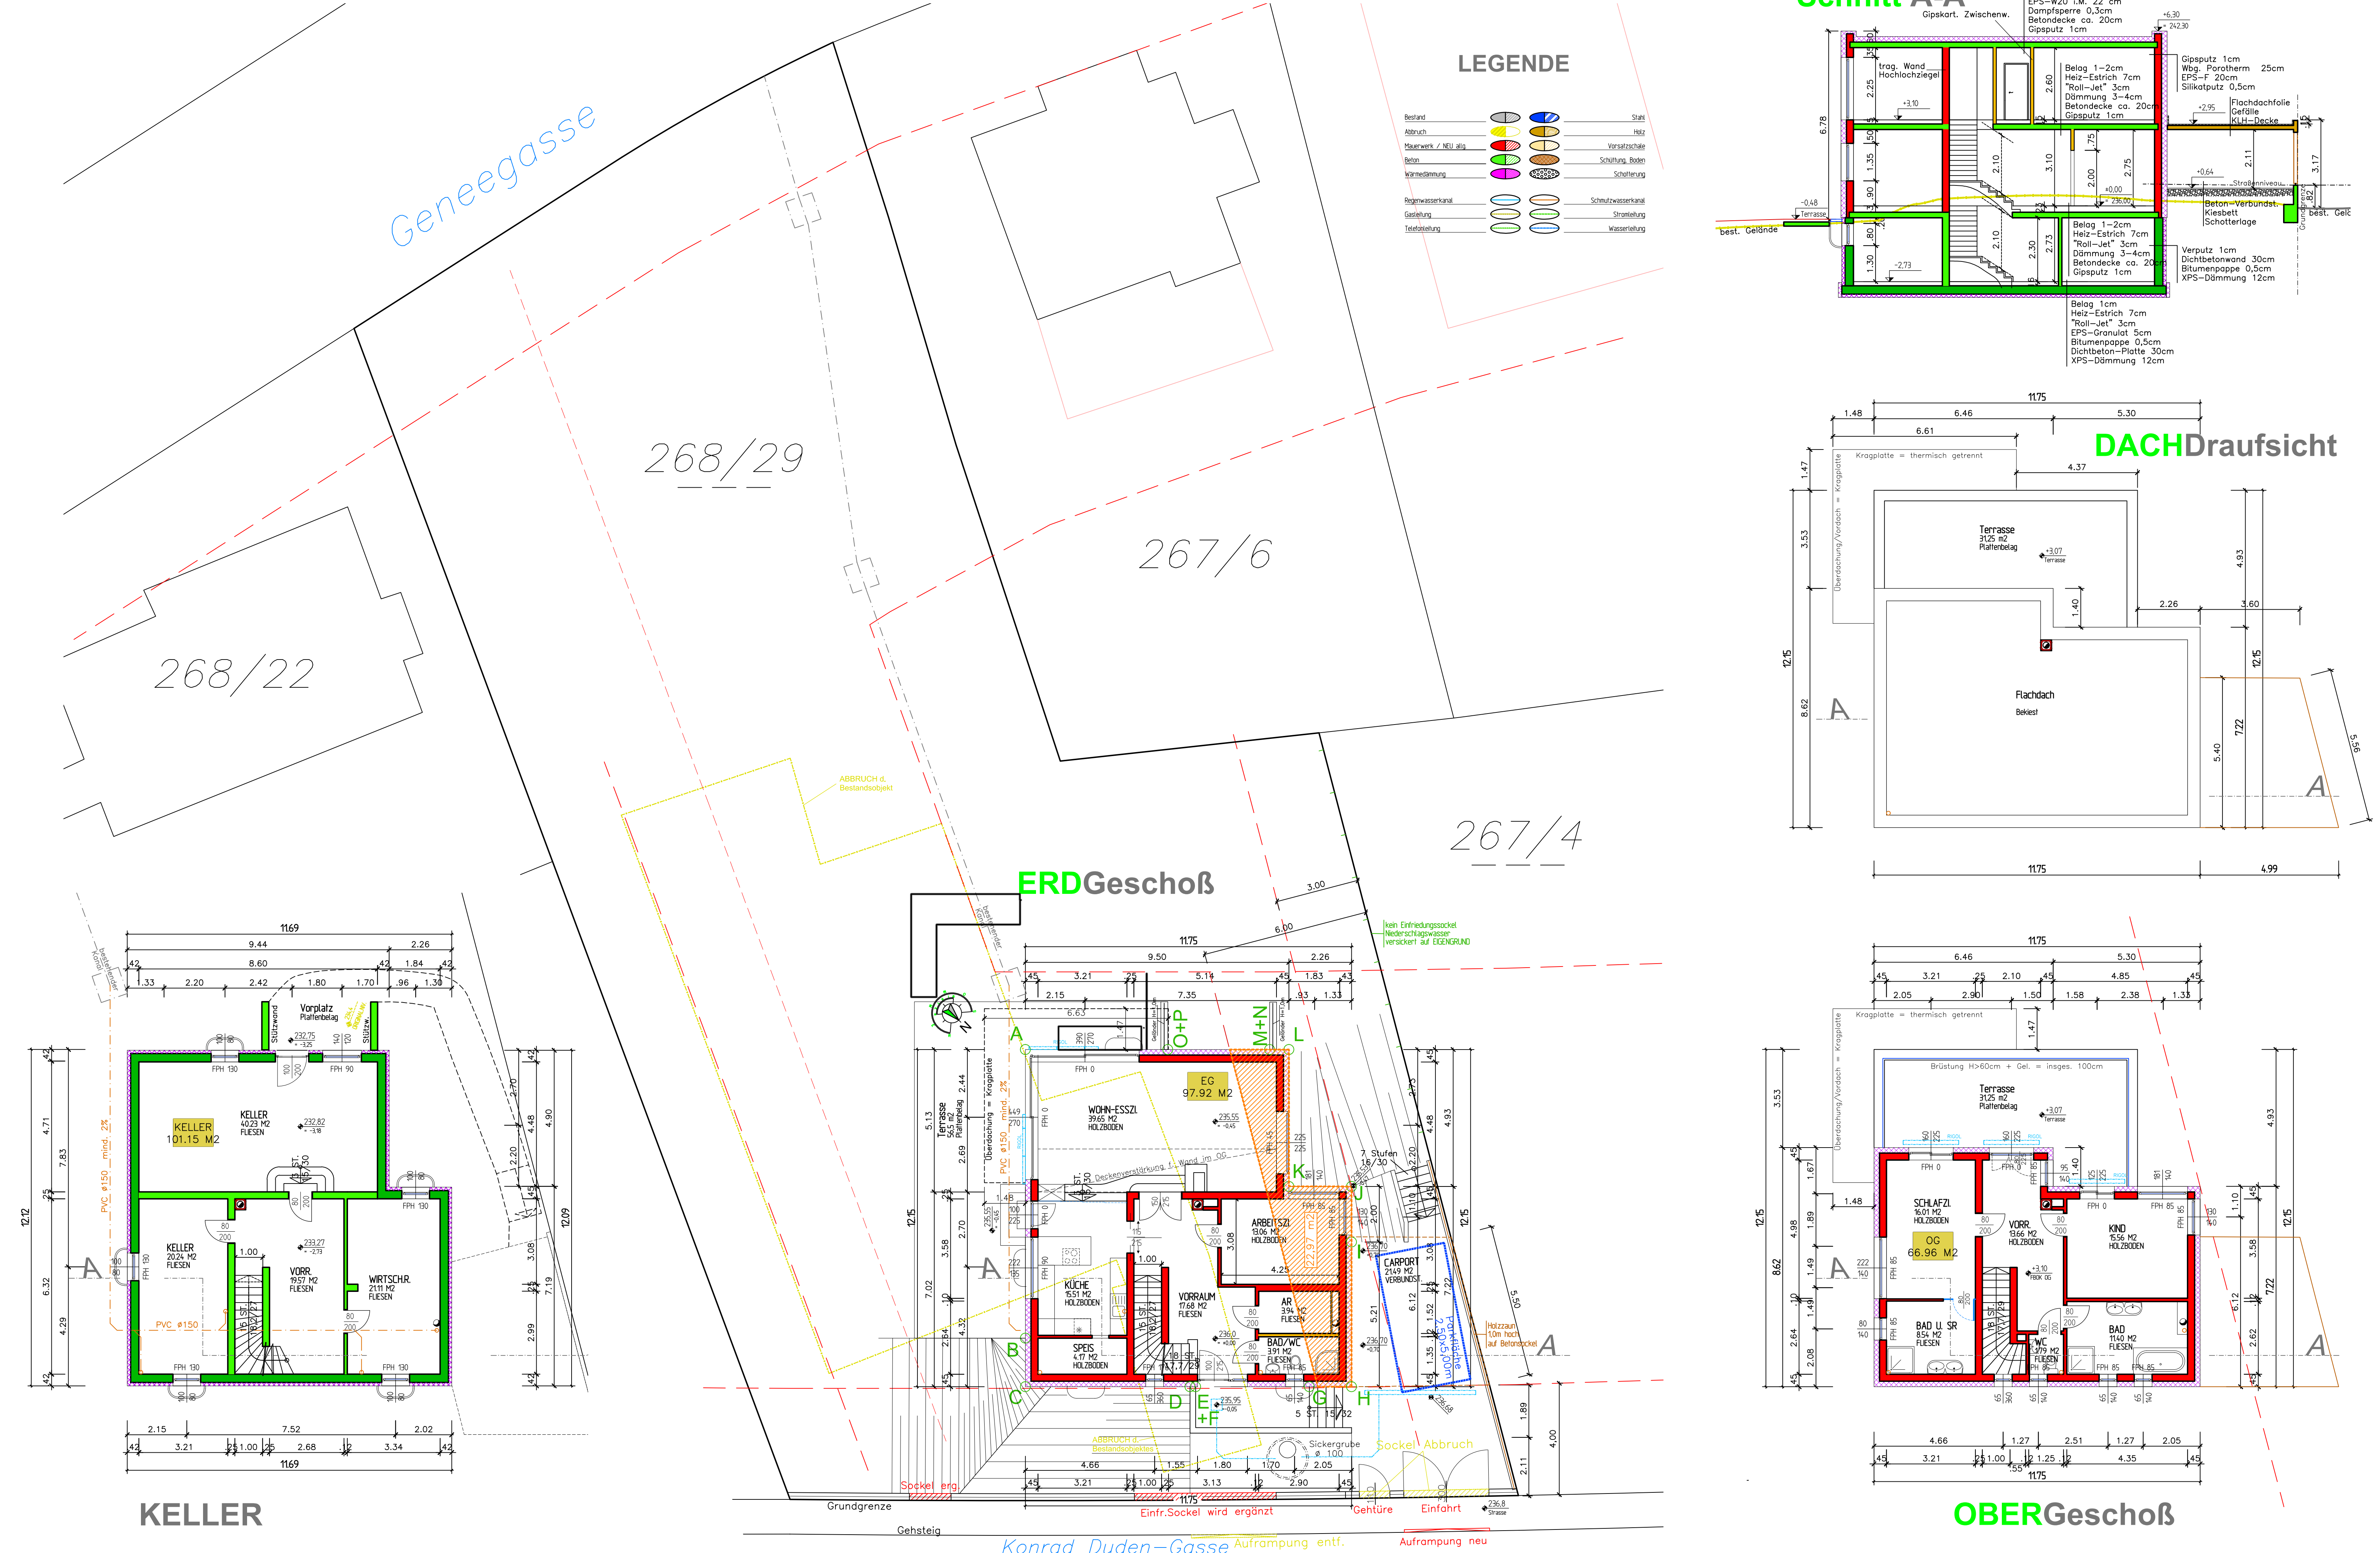
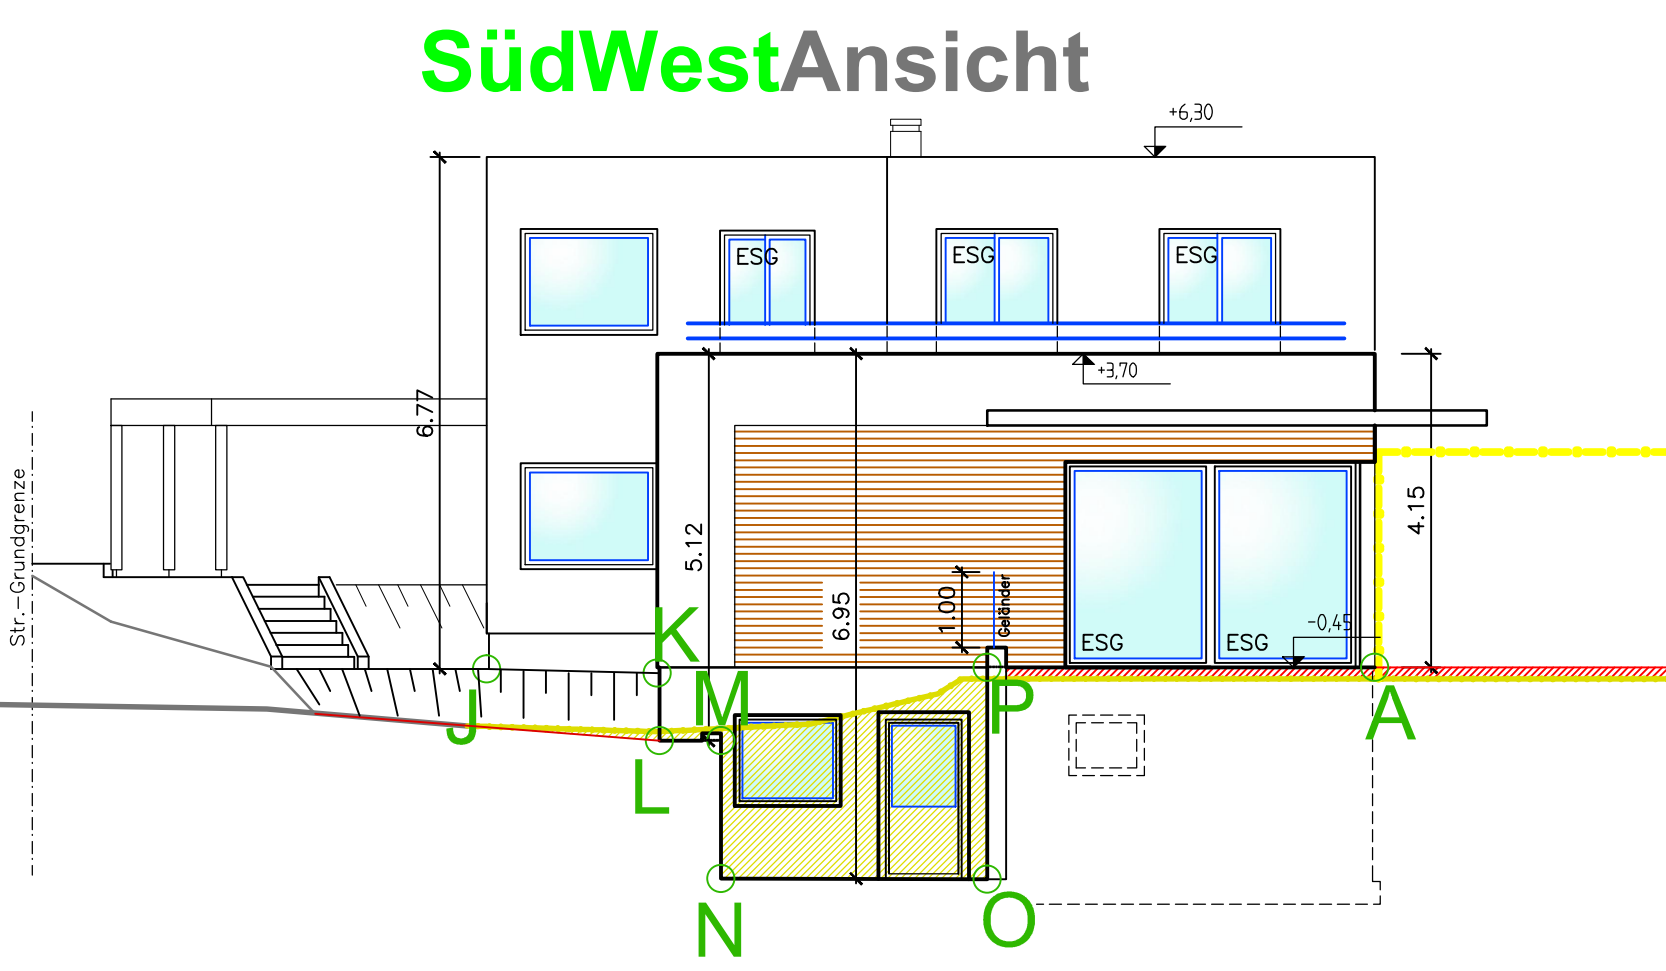
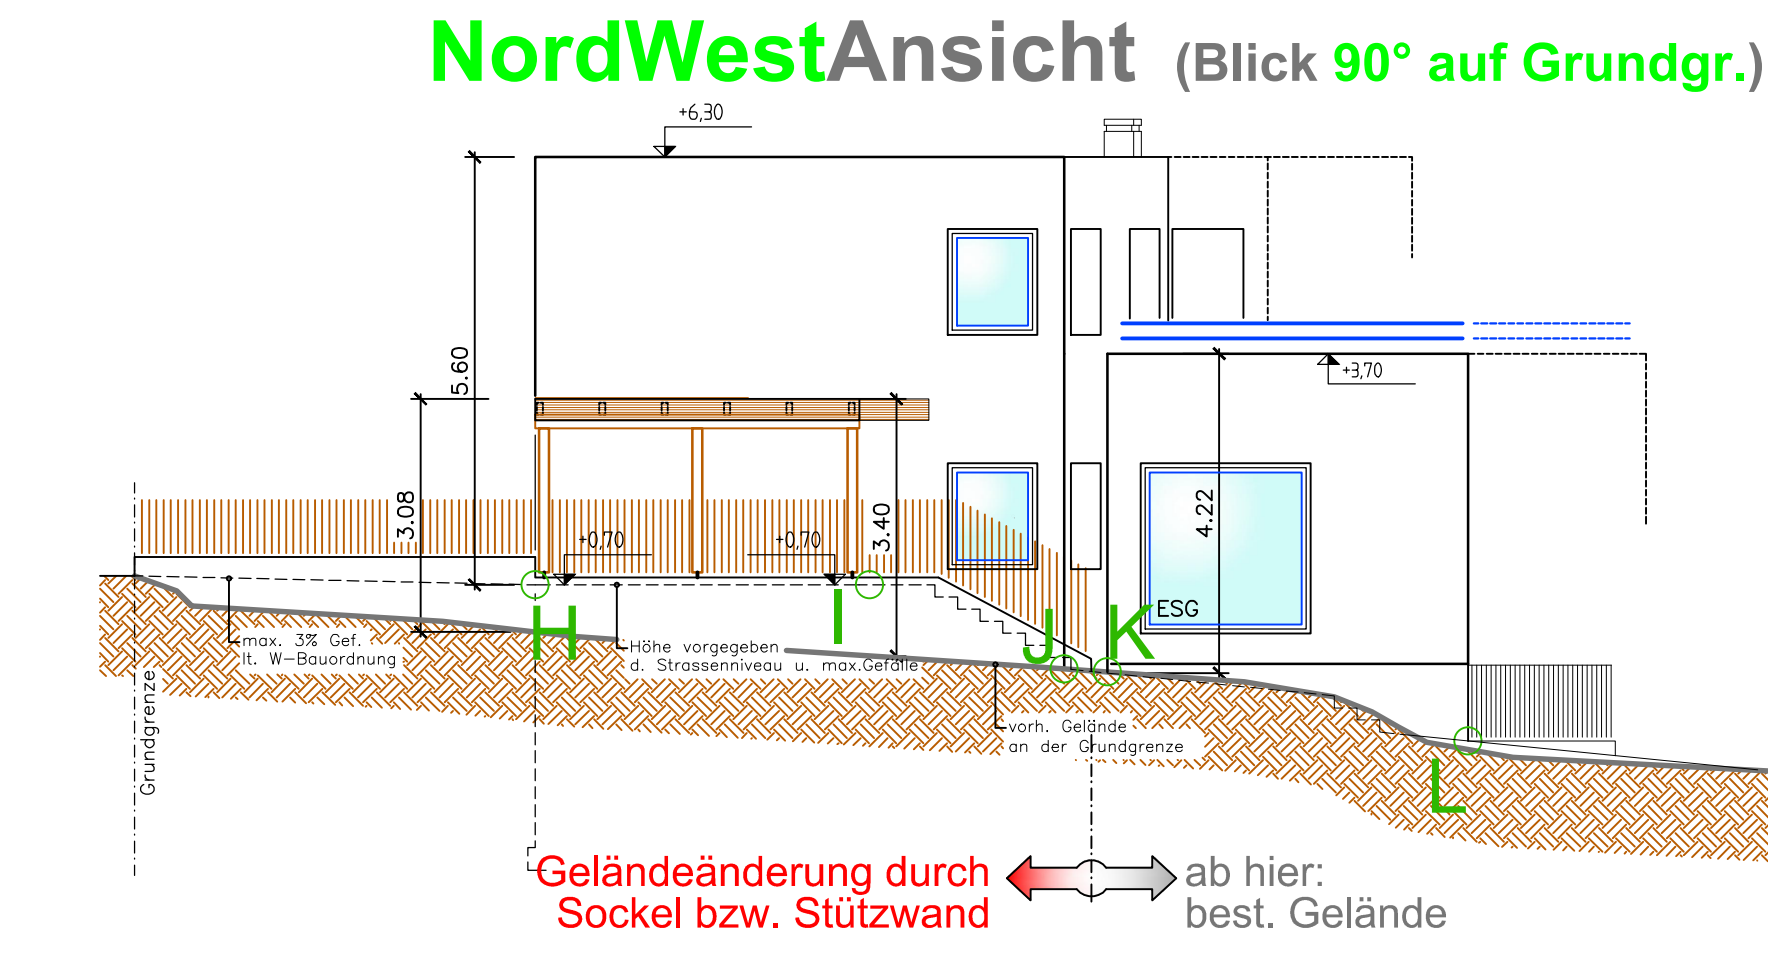
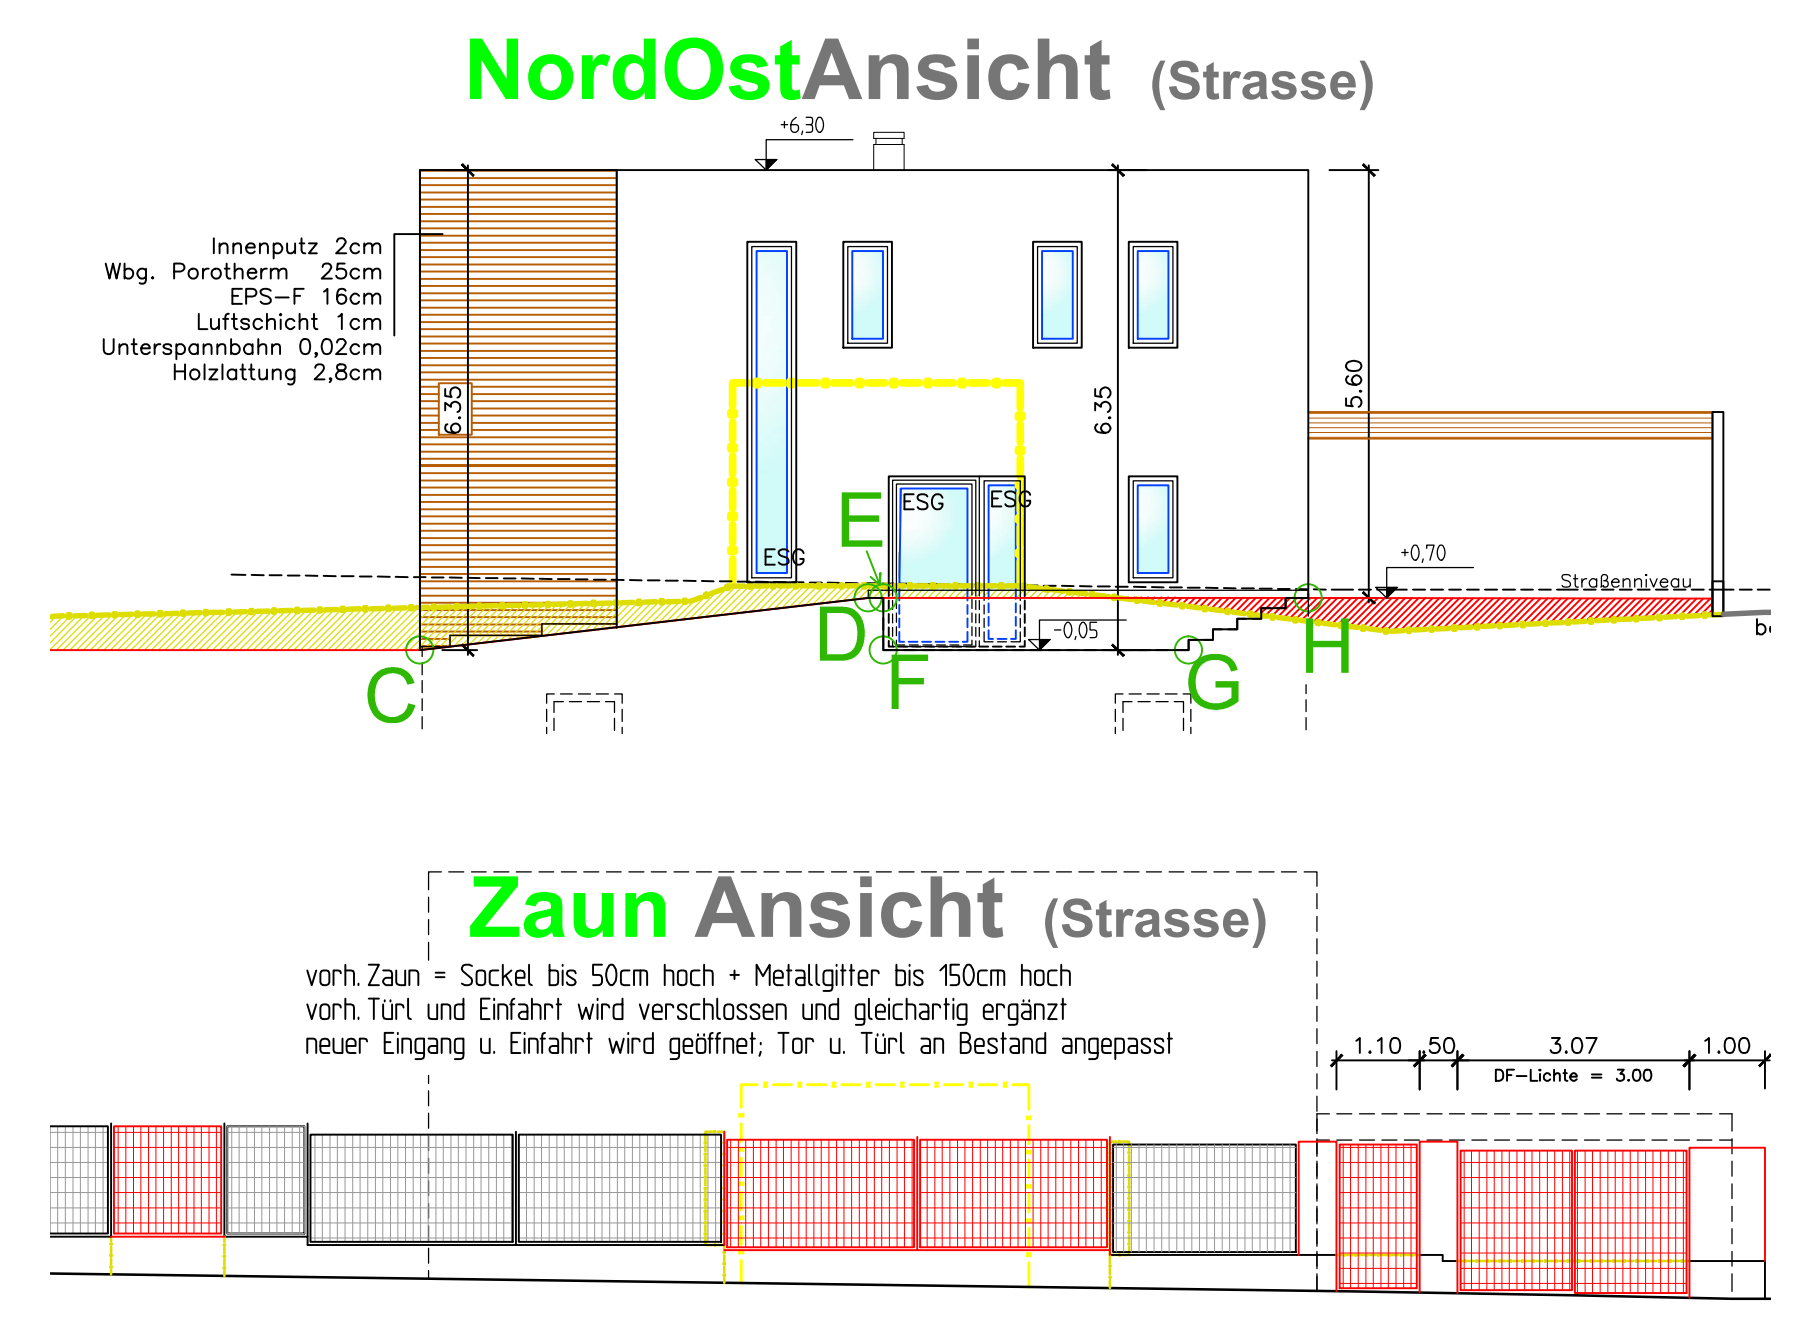
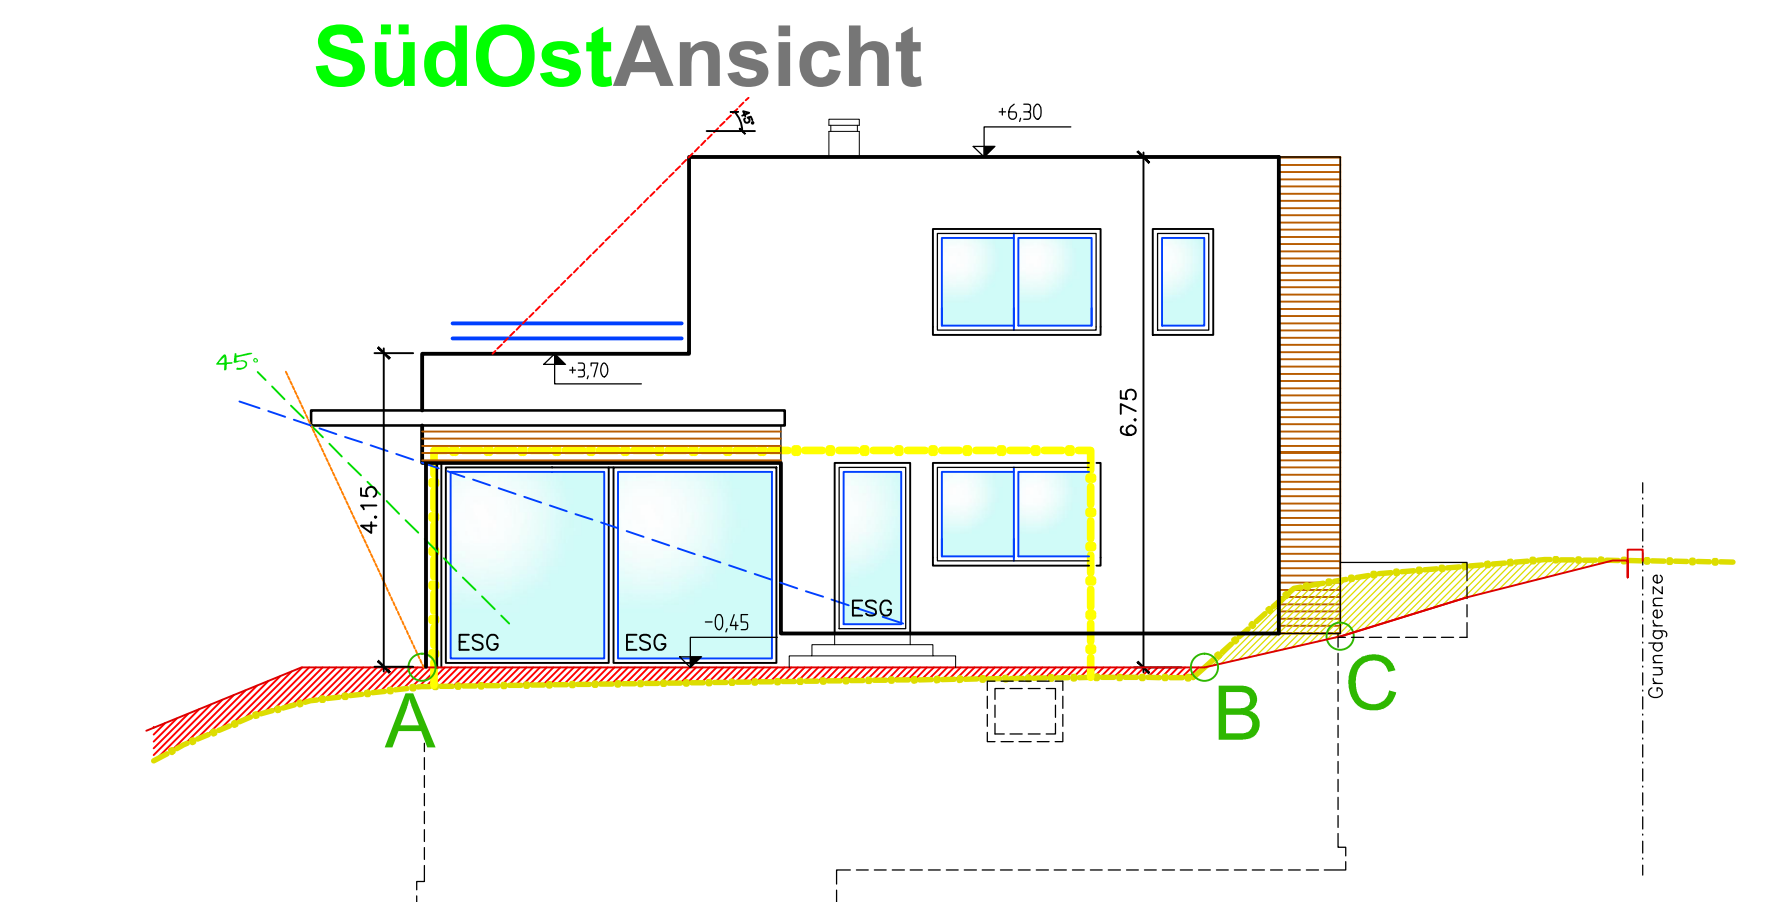
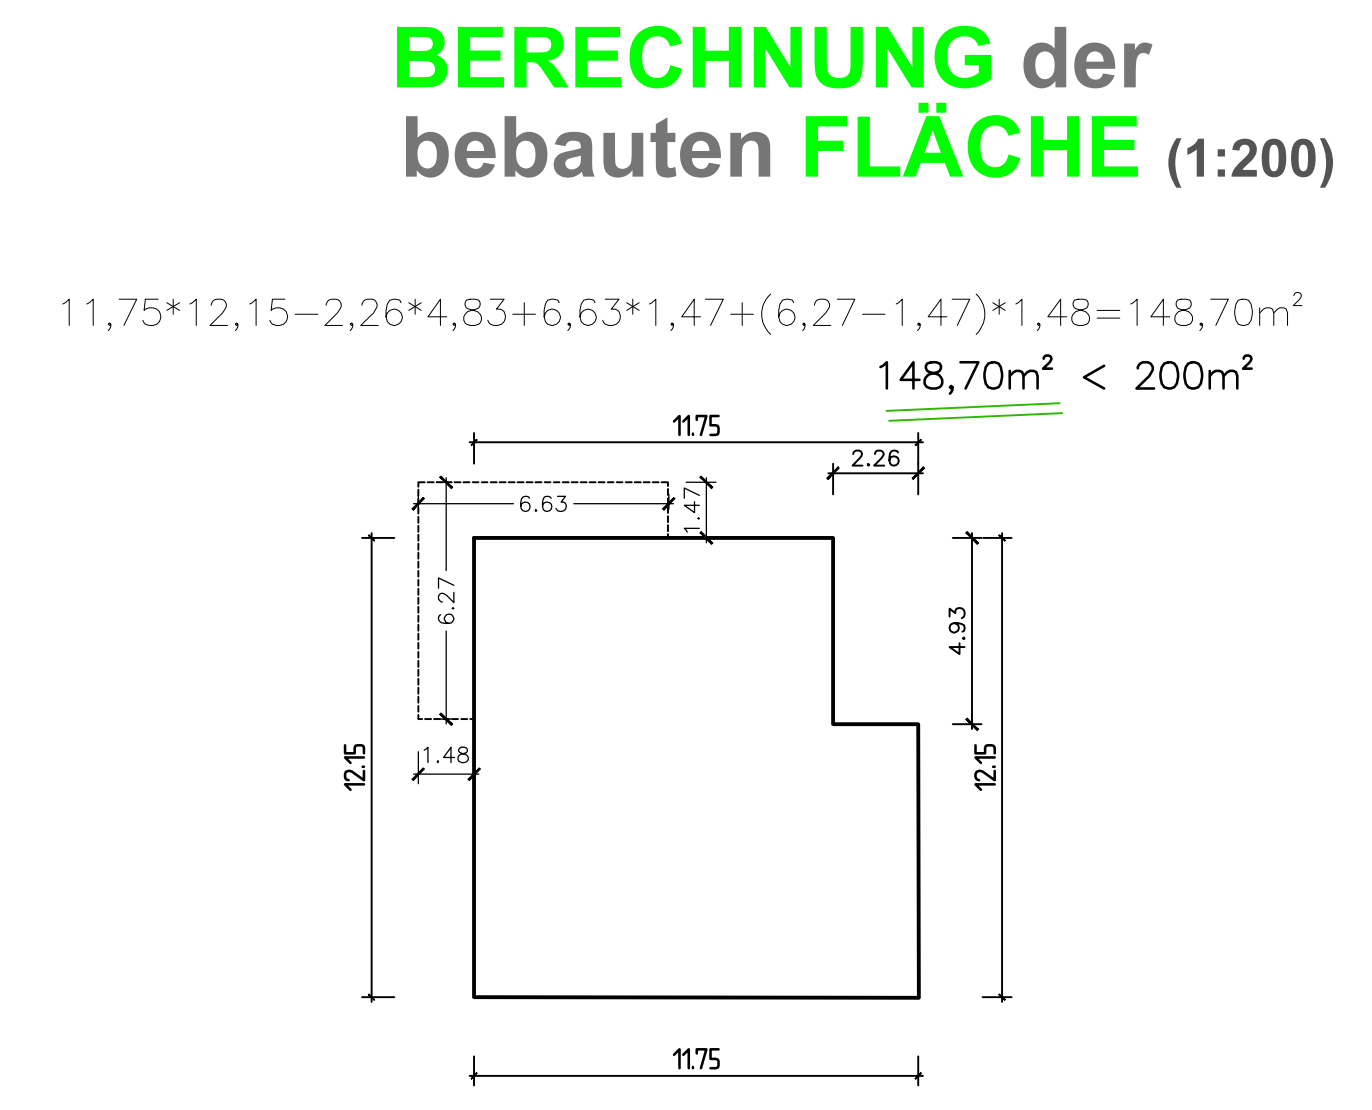
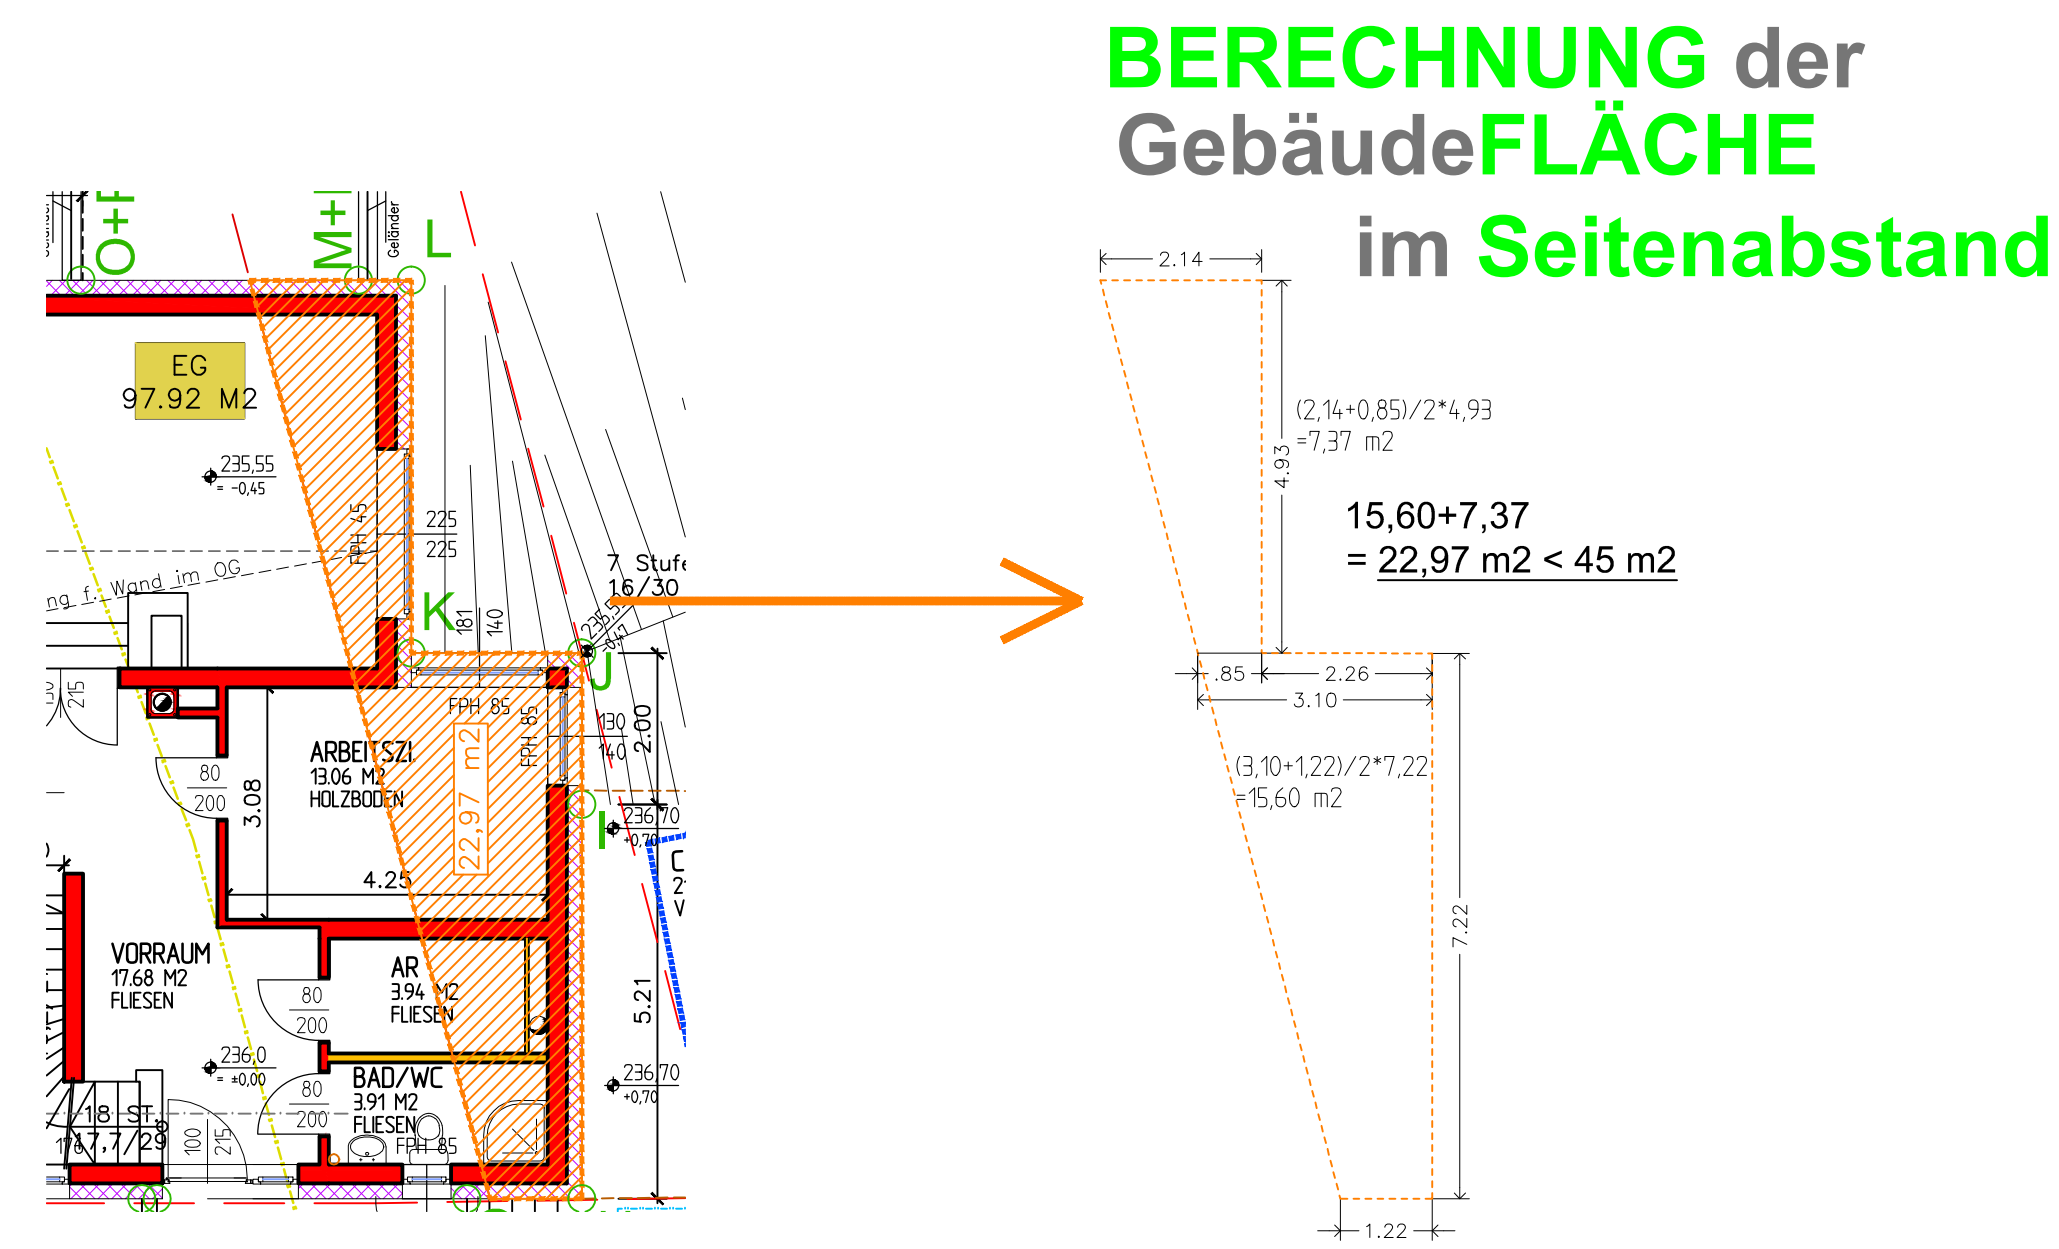


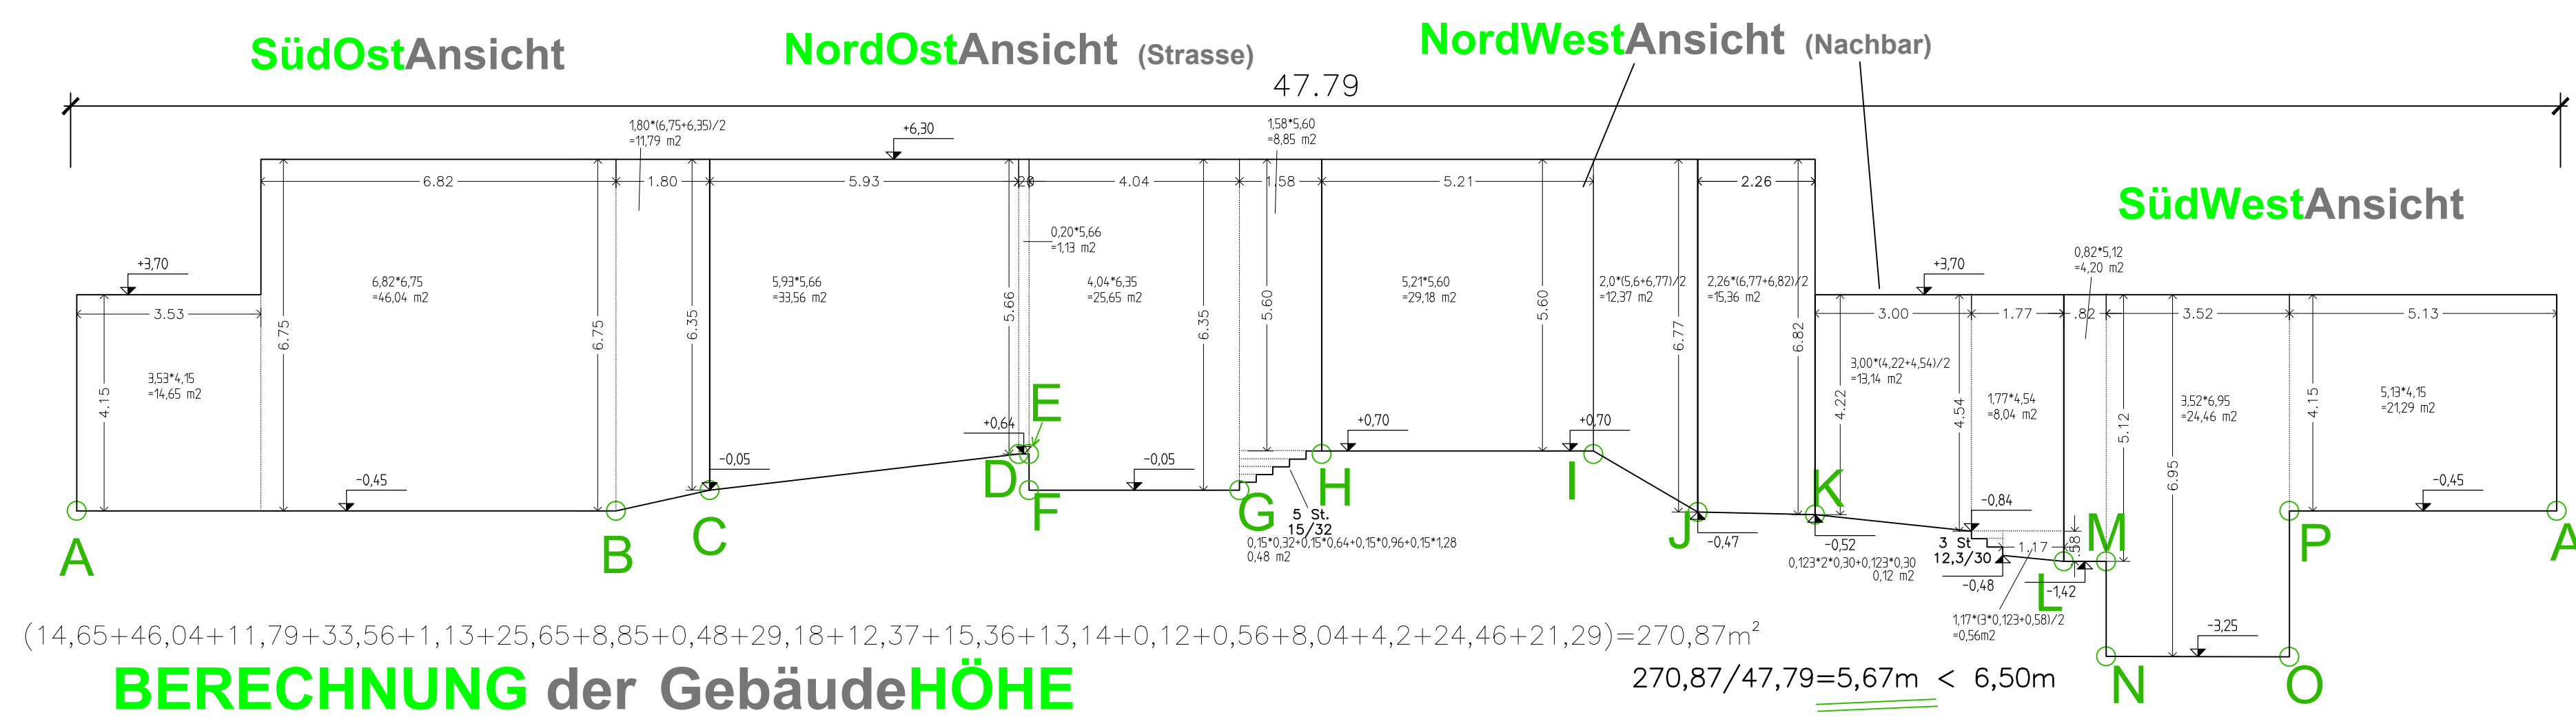

**EINREICHPLAN**

**BAUVORHABEN**

**Wohnhaus m. Carport**

in Wien, Konrad Duden Gasse 11  
GST 268/29 - EZ 1072 - KG 01207 Lainz

**BAUWERBER**

Elena u. Johannes Dobler  
Fasangartengasse 3/7  
1130 WIEN

**BEHÖRDE / GENEHMIGUNGSVERMERK**

**BAUWERBER = GRUNDEIGENTÜMER**

J. Dobler

**PLAN-NR.**

18 1319

**DATUM**

22.09.2018  
erstellt von: M. B. M.

**INDEX / ÄNDERUNG / ANMERKUNG**

**PLANVERFASSER**

ING. WERNER KOIZAR GmbH  
Planung, Bauleitung, Baustellenkoordination  
8340 BAD VÖLLAU, HAUPTBEREICH 1 TEL: 02255 704000 MAIL: OFFICE@KOIZAR.AT WEB: WWW.KOIZAR.AT